


2 PANTRY 310 - PLAN VIEW

Scale: 1"=1'-0"

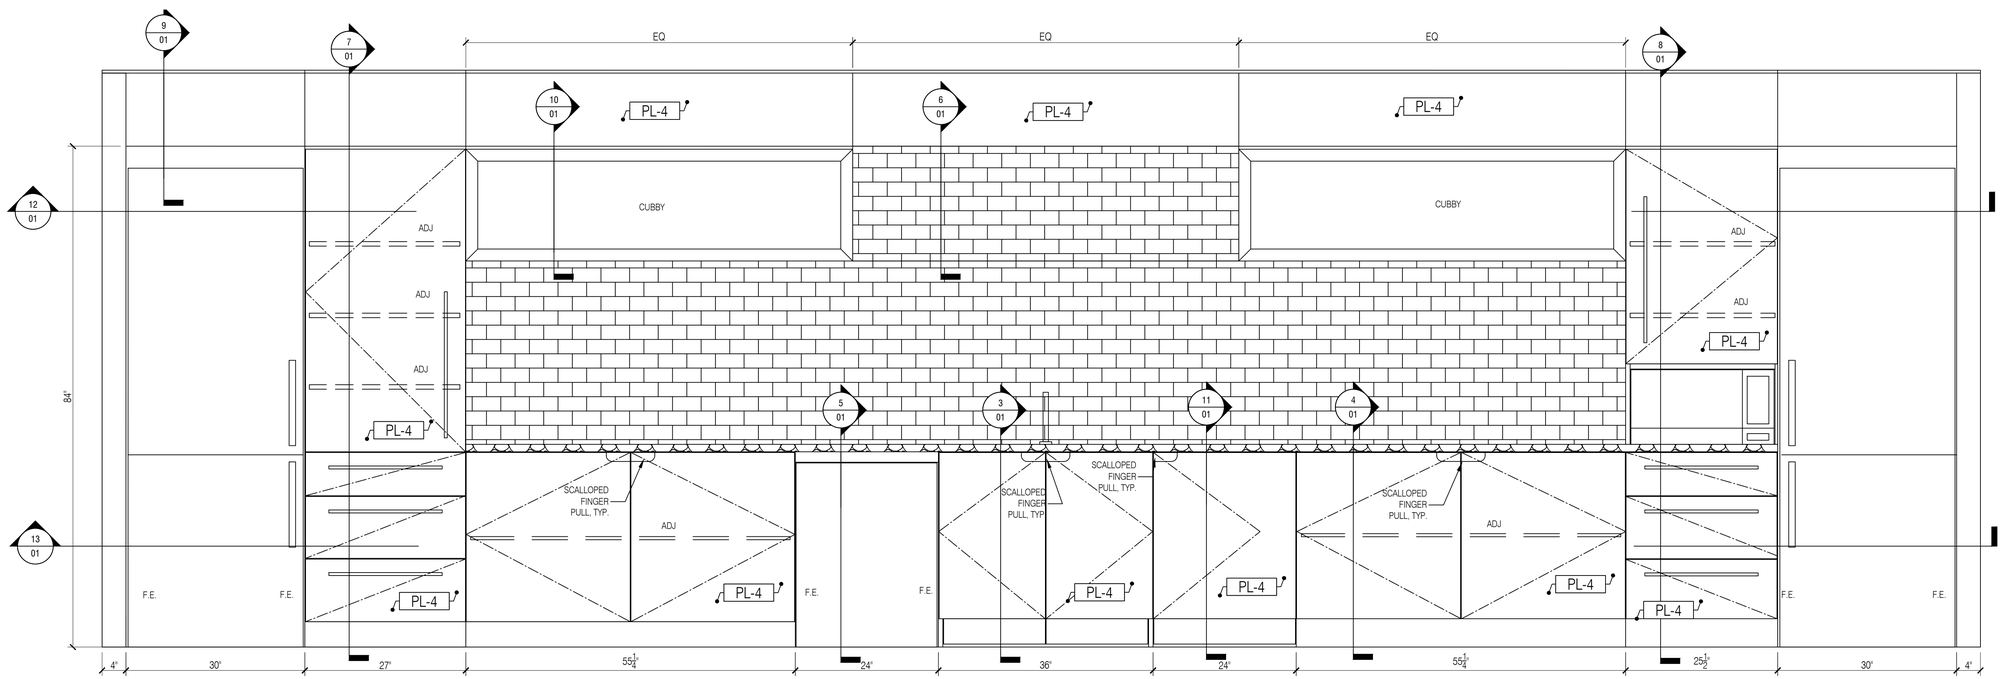

2 PANTRY 310 - ELEVATION

Scale: 1"=1'-0"

NO:	REVISIONS:	NAME:	DATE:
1	SUBMISSION FOR APPROVAL	A.Y.	04/12/2022
2	REVISED AS PER COMMENTS	A.Y.	05/10/2022

BESTMARK
NATIONAL LLC
171 COIT STREET
IRVINGTON, NJ 07111
TEL. 862-772-4863
FAX. 973-849-6140
info@bestmarknational.com

WEWORK HOWELL MILL RD - 5TH FLOOR
1115 HOWELL MILL RD NW
ATLANTA, GA 30318

DATE : 04/12/2022

DRAWN BY : A.Y.

ARCHITECT :
LITTLE
615 SOUTH COLLEGE STREET, SUITE 1600, CHARLOTTE, NC 28202


CONTRACTOR :

DRAWING TITLE :
PANTRY 310
PLAN


ROOM OR SPACE : FLOOR : 310

PROJECT NUMBER: 050-22


DRAWING NUMBER: 01

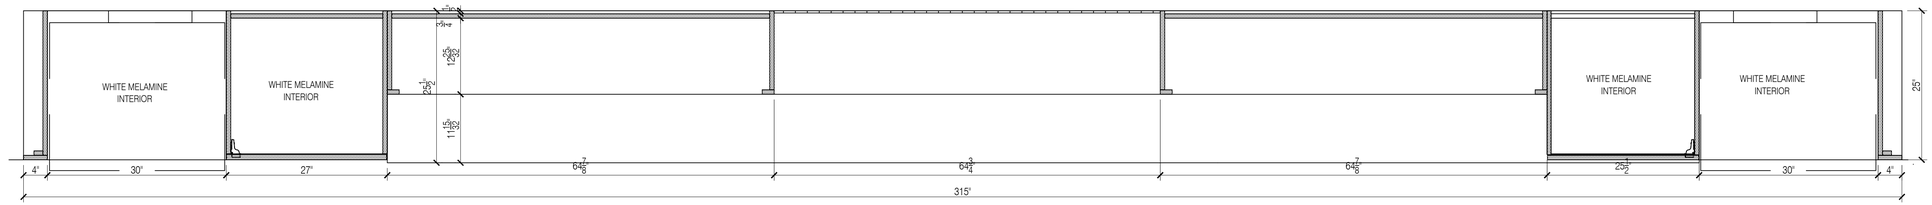


12 PANTRY 310 - PLAN SECTION
Scale: 1"=1'-0"

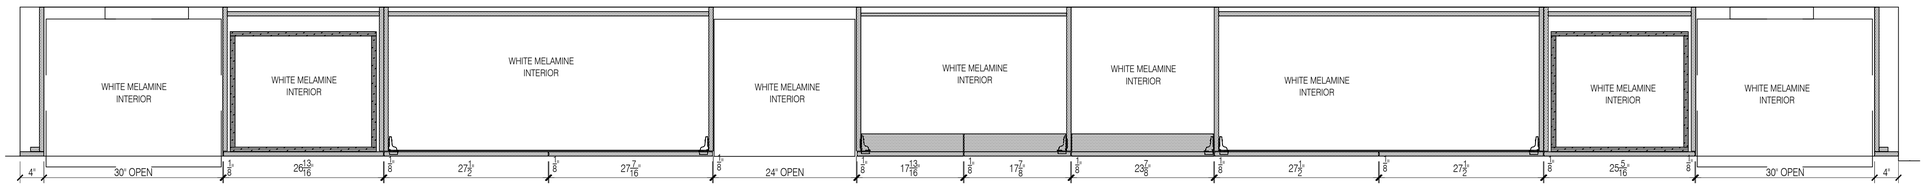


13 PANTRY 310 - PLAN SECTION
Scale: 1"=1'-0"

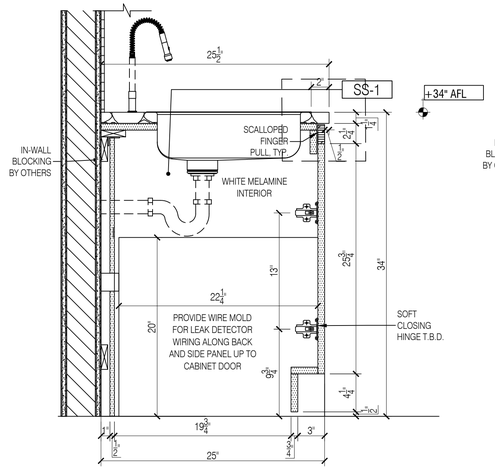


3 PANTRY - SECTION
Scale: 1-1/2"=1'-0"

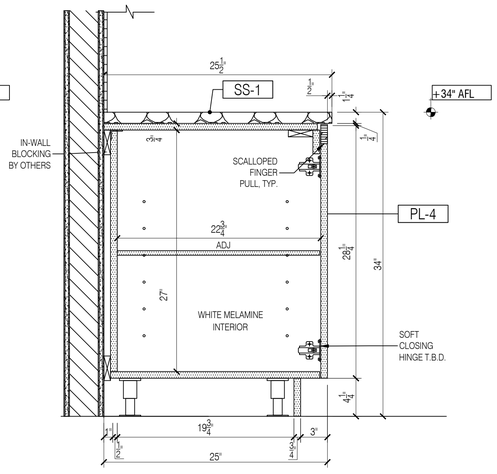

4 PANTRY - SECTION
Scale: 1-1/2"=1'-0"

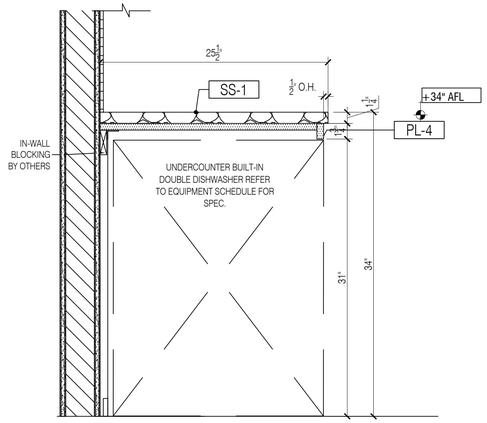

5 PANTRY - SECTION
Scale: 1-1/2"=1'-0"

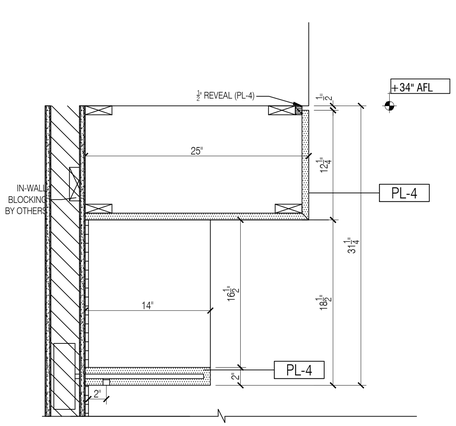


6 PANTRY - SECTION
Scale: 1-1/2"=1'-0"

NO:	REVISIONS:	NAME:	DATE:
1	SUBMISSION FOR APPROVAL	A.Y.	04/12/2022
2	REVISED AS PER COMMENTS	A.Y.	05/10/2022


BESTMARK
NATIONAL LLC
171 COIT STREET
IRVINGTON, NJ 07111
TEL. 862-772-4863
FAX. 973-849-6140
info@bestmarknational.com

WEWORK HOWELL MILL RD - 5TH FLOOR
1115 HOWELL MILL RD NW
ATLANTA, GA 30318


DATE : 04/12/2022
DRAWN BY : A.Y.
ARCHITECT : LITTLE
615 SOUTH COLLEGE STREET, SUITE 1300, CHARLOTTE, NC 28202
CONTRACTOR :
DRAWING TITLE : PANTRY 310 PLANS
ROOM OR SPACE : FLOOR : 310
PROJECT NUMBER: 050-22
DRAWING NUMBER: 02

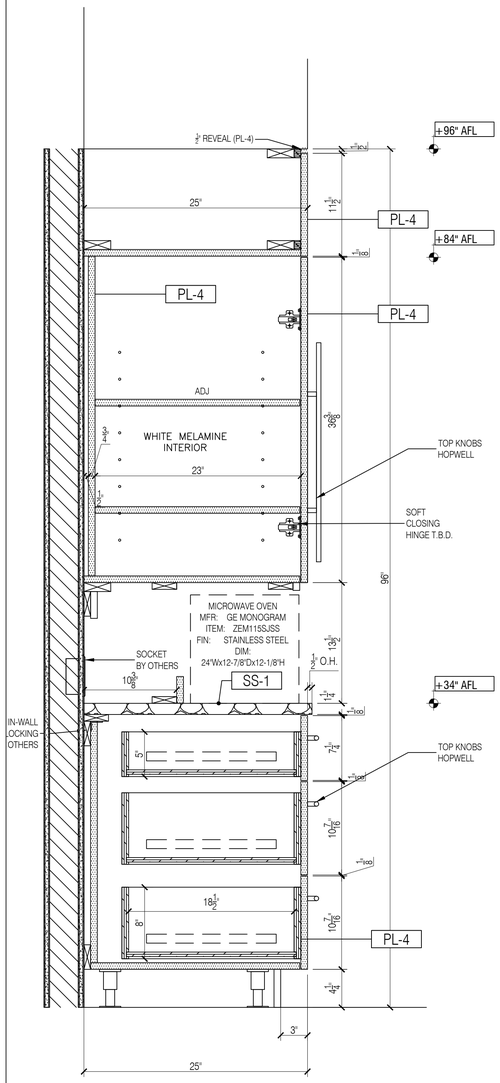


7 PANTRY - SECTION
Scale: 1-1/2"=1'-0"

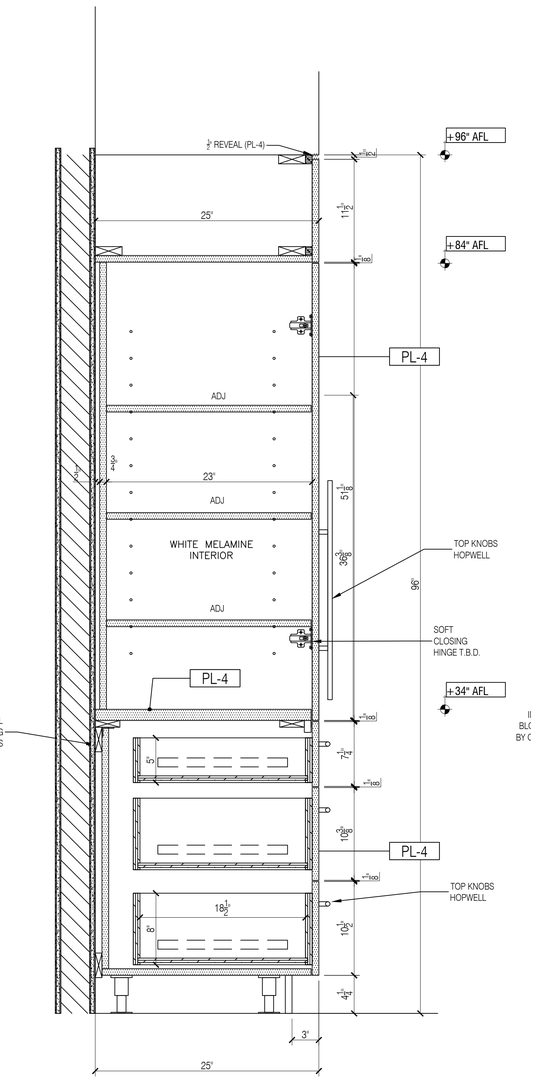


8 PANTRY - SECTION
Scale: 1-1/2"=1'-0"

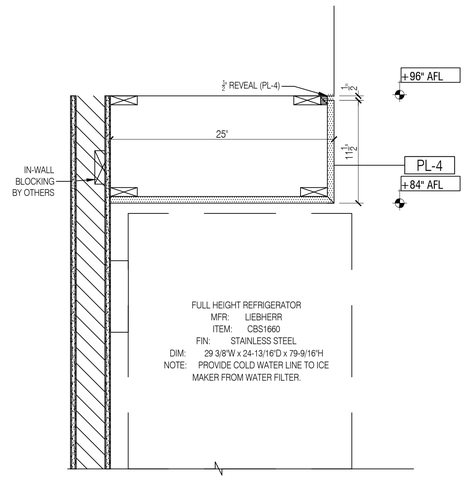


9 PANTRY - SECTION
Scale: 1-1/2"=1'-0"

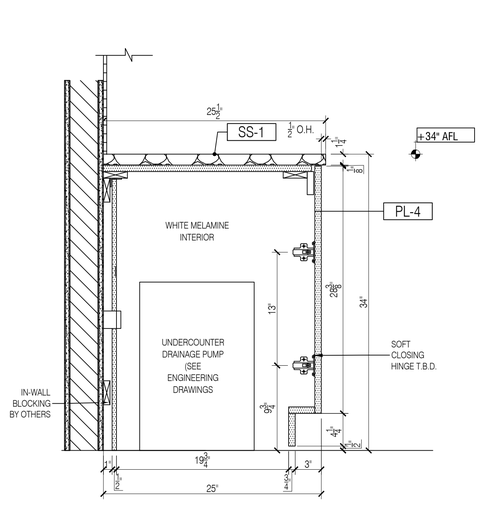

11 PANTRY - SECTION
Scale: 1-1/2"=1'-0"

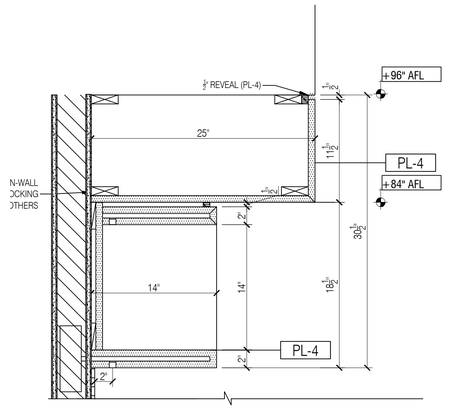

10 PANTRY - SECTION
Scale: 1-1/2"=1'-0"

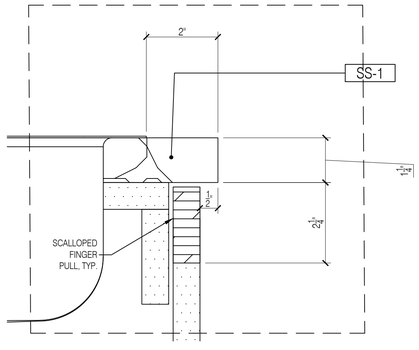

D DETAIL
Scale: 6"=1'-0"

NO:	REVISIONS:	NAME:	DATE:
1	SUBMISSION FOR APPROVAL	A.Y.	04/12/2022
2	REVISED AS PER COMMENTS	A.Y.	05/10/2022

BESTMARK
NATIONAL LLC
171 COIT STREET
IRVINGTON, NJ 07111
TEL. 862-772-4863
FAX. 973-849-6140
info@bestmarknational.com

WEWORK HOWELL MILL RD - 5TH FLOOR
1115 HOWELL MILL RD NW
ATLANTA, GA 30318

DATE : 04/12/2022
DRAWN BY : A.Y.
ARCHITECT : LITTLE
615 SOUTH COLLEGE STREET, SUITE 1900, CHARLOTTE, NC 28202
CONTRACTOR :
DRAWING TITLE : PANTRY 310 PLAN
ROOM OR SPACE : FLOOR : 310
PROJECT NUMBER: 050-22
DRAWING NUMBER: 03