


1/36 PLAN @ PT ROOM 00023

2/36


SCALE: 1"=1'-0"

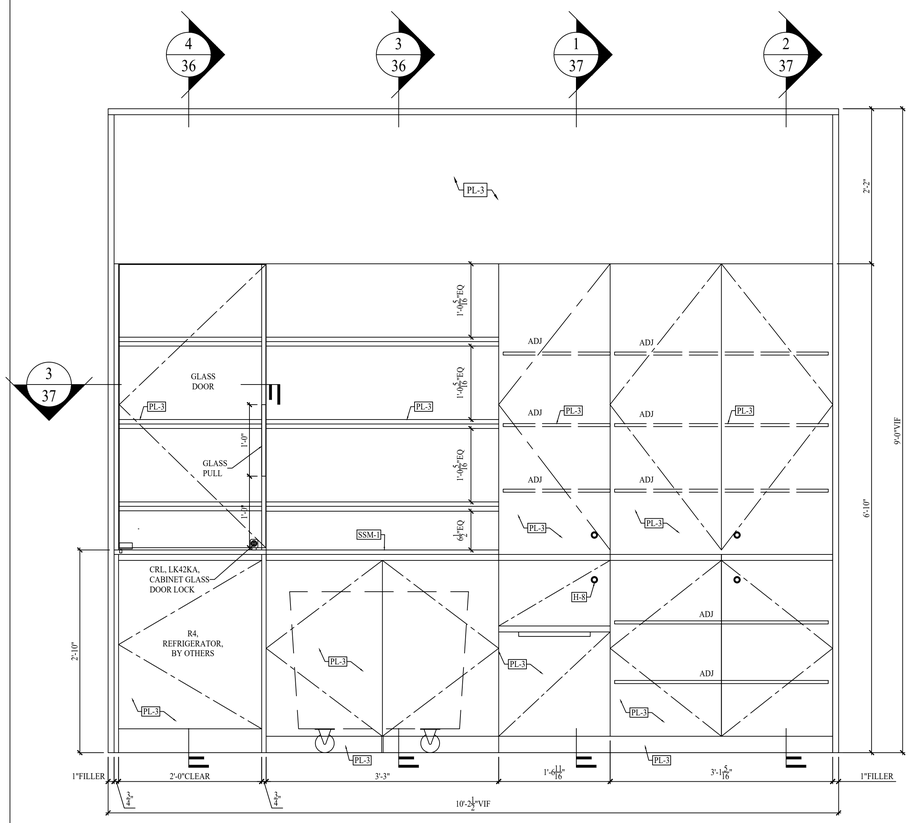

3/37


2/36 ELEVATION @ PT ROOM 00023

SCALE: 1"=1'-0"

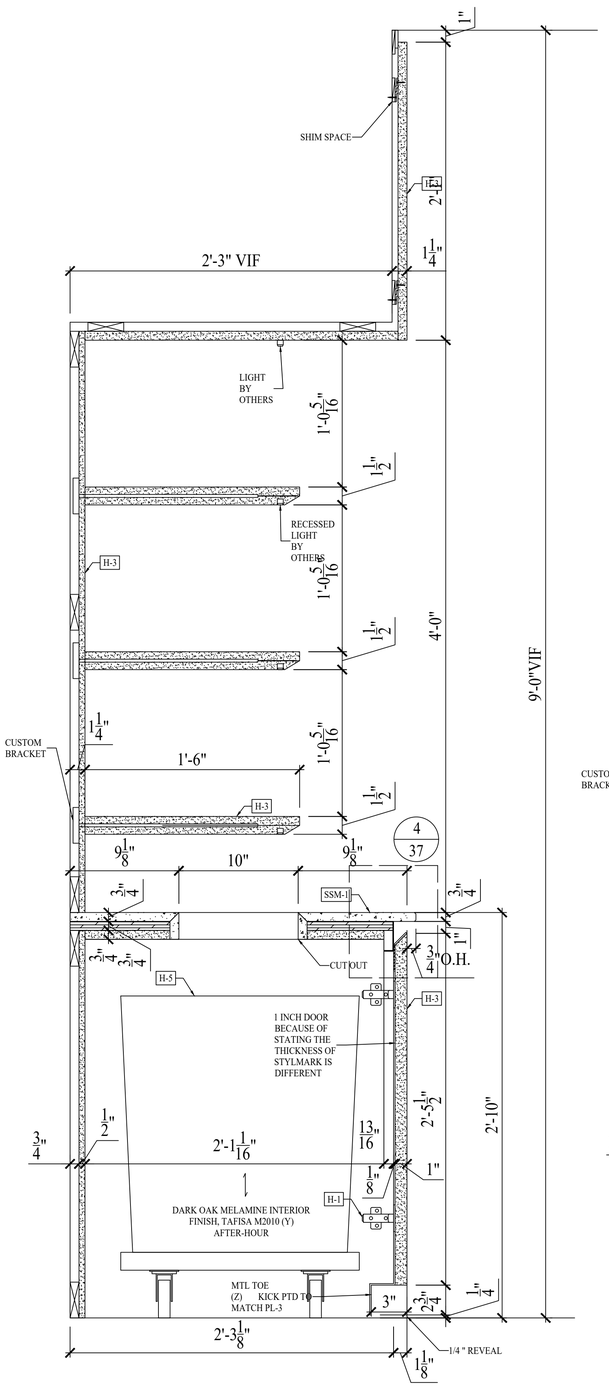

3/36 VERTICAL SECTION

SCALE: 2"=1'-0"

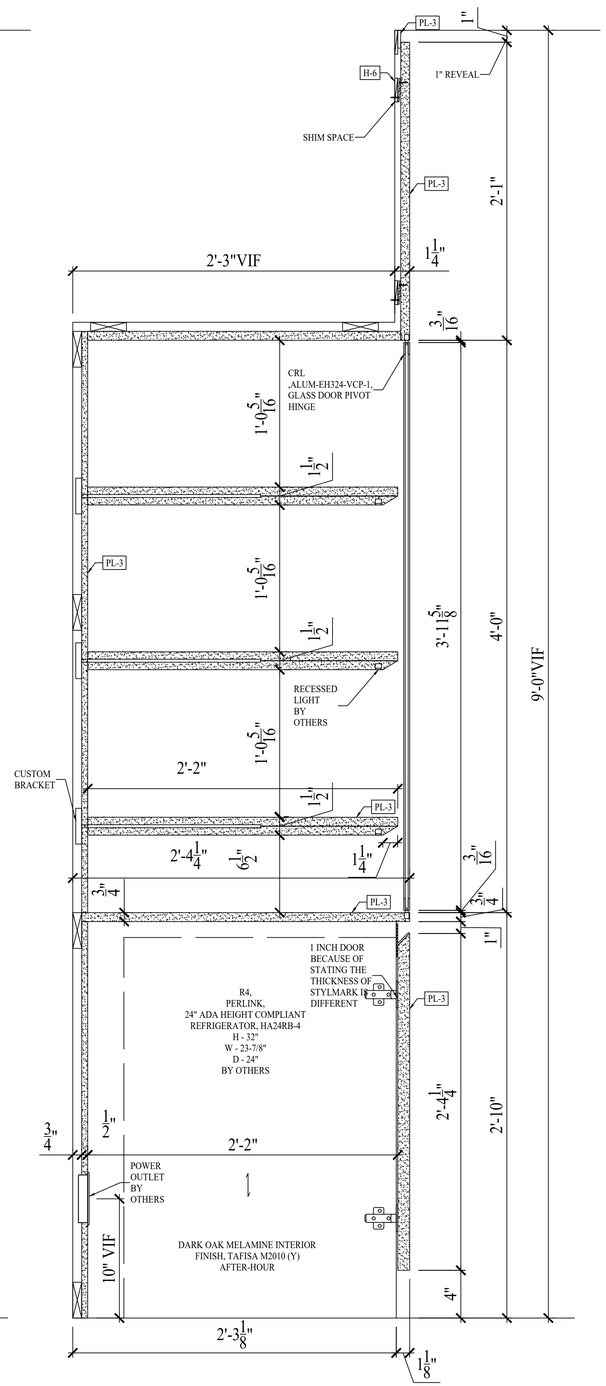

4/36 VERTICAL SECTION

SCALE: 2"=1'-0"

PLASTIC LAMINATE

PL-1	ARPA, 4521 – FRASSINO AMERICANO, ERRE FINISH
PL-2	WILSONART HPL, "FROSTY WHITE" MATTE FINISH (60) #1573-60
PL-3	WILSONART HPL, "FROSTY WHITE" MATTE FINISH (60) #1573-60

WOOD SPECIES

FINISHES

SOLID SURFACES

SSM-1	CORIAN 'GLACIER WHITE', MATTE FINISH

HARDWARE

H-1	HEAVY DUTY CONCEALED HINGE, TBD
H-2	BLUM, TIP-ON TOUCH LATCH, 956A1006
H-3	HAFELE, WASTE BIN DRW, HAILO EURO CARGO 45
H-4	NEXT LOCK, MECHANICAL LOCK, DS-NLMD-DEN
H-5	ULINE, H-1806 BASKET TRUCK, BLACK
H-6	Z-CLIPS, TBD
H-7	OVAL CLOSET ROD CHROME, TBD
H-8	LOCK, TBD
H-9	STYLMARK, ANGLE, 110293. BRUSHED SATIN NATURAL 120 FINISH
H-10	STYLMARK, FLAT BAR, 111095. BRUSHED SATIN NATURAL 120 FINISH
H-11	STYLMARK, ANGLE, 110306. BRUSHED SATIN NATURAL 120 FINISH
H-12	STYLMARK, ANGLE, 110997. BRUSHED SATIN NATURAL 120 FINISH
H-13	FLAP HINGE, HÄFELE MINIFIX, 90°, FOR WOODEN FLAPS

MISCELLANEOUS

MTL-3	PAINTED ALUMINUM, TIGER DRYLAC POWDER COATING, SATIN FINISH, COLOR TO MATCH P#1

EXCLUSIONS

EX-1	GLASS
EX-2	HARDWARE
EX-3	STAINLESS STEEL
EX-4	STONE
EX-5	FABRIC
EX-6	METAL TRIMS & METAL GRILLES
EX-7	LIGHTING FIXTURES
EX-8	LEATHER
EX-9	MIRRORS

☐ APPROVED / NO CHANGES

☐ APPROVED / AS NOTED

☐ REVISE AS NOTED / RESUBMIT

X SIGNATURE

DATE

INTERIOR WOODWORK INSTALLATION

118 JOHNSON St.
Newark, N.J. 07114
Tel: 973-621-9595
Fax: 973-621-0395

PROJECT:

MILLENIUM
399 PARK AVENUE
NEW YORK, NY 10022

TITLE:


SCALE: AS NOTED	No:	DATE:	REVISION:
DATE: 12-20-21	1	01-19-22	CGI
DRAWN BY: M.V.			
CHK BY:			

ARCHITECT: LSM

ARCHITECTURAL DRAWING DATE: 11/24/2021 ADDENDUM #1


GC: PETRETTI

DWG#: 36

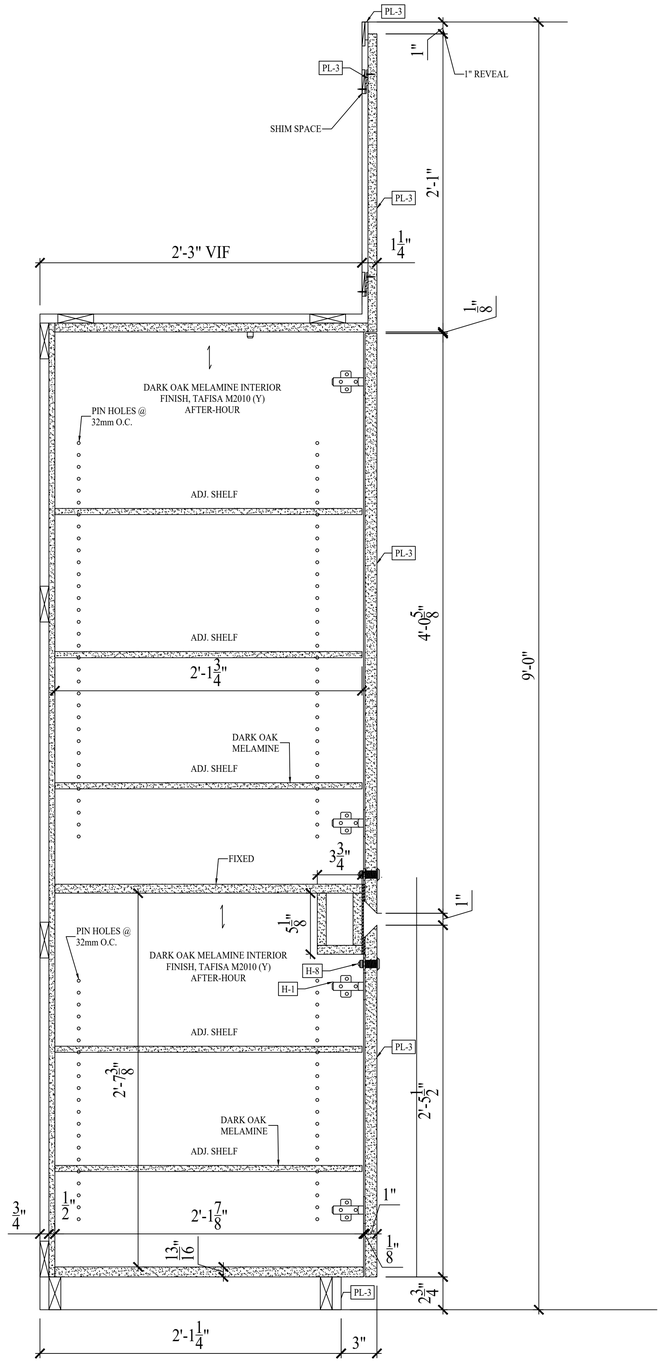


1 / 37 VERTICAL SECTION

SCALE: 2"=1'-0"

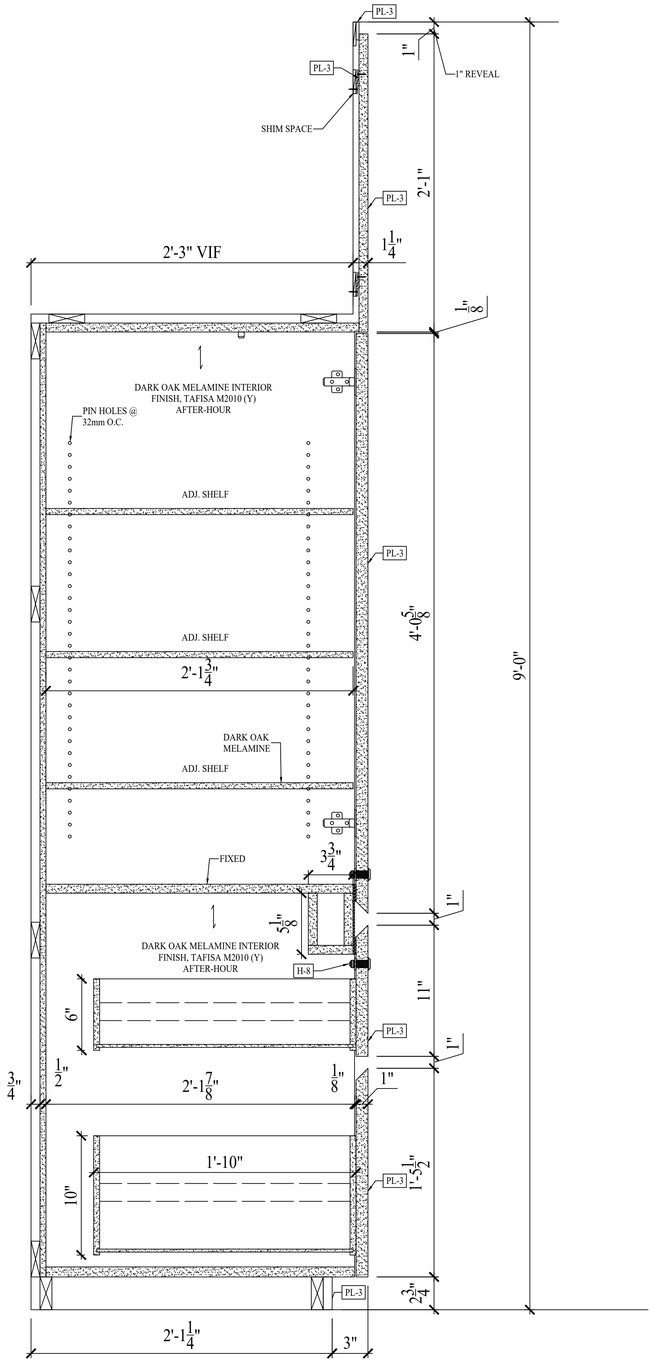


2 / 37 VERTICAL SECTION

SCALE: 2"=1'-0"

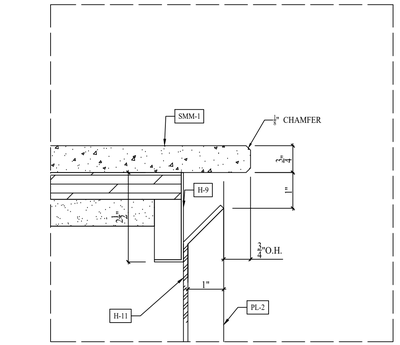

4 / 37 DETAIL

SCALE: 6"=1'-0"

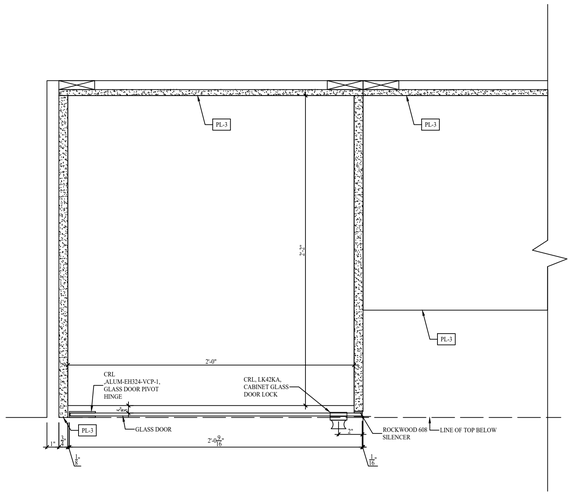

3 / 37 HORIZONTAL SECTION

SCALE: 2"=1'-0"